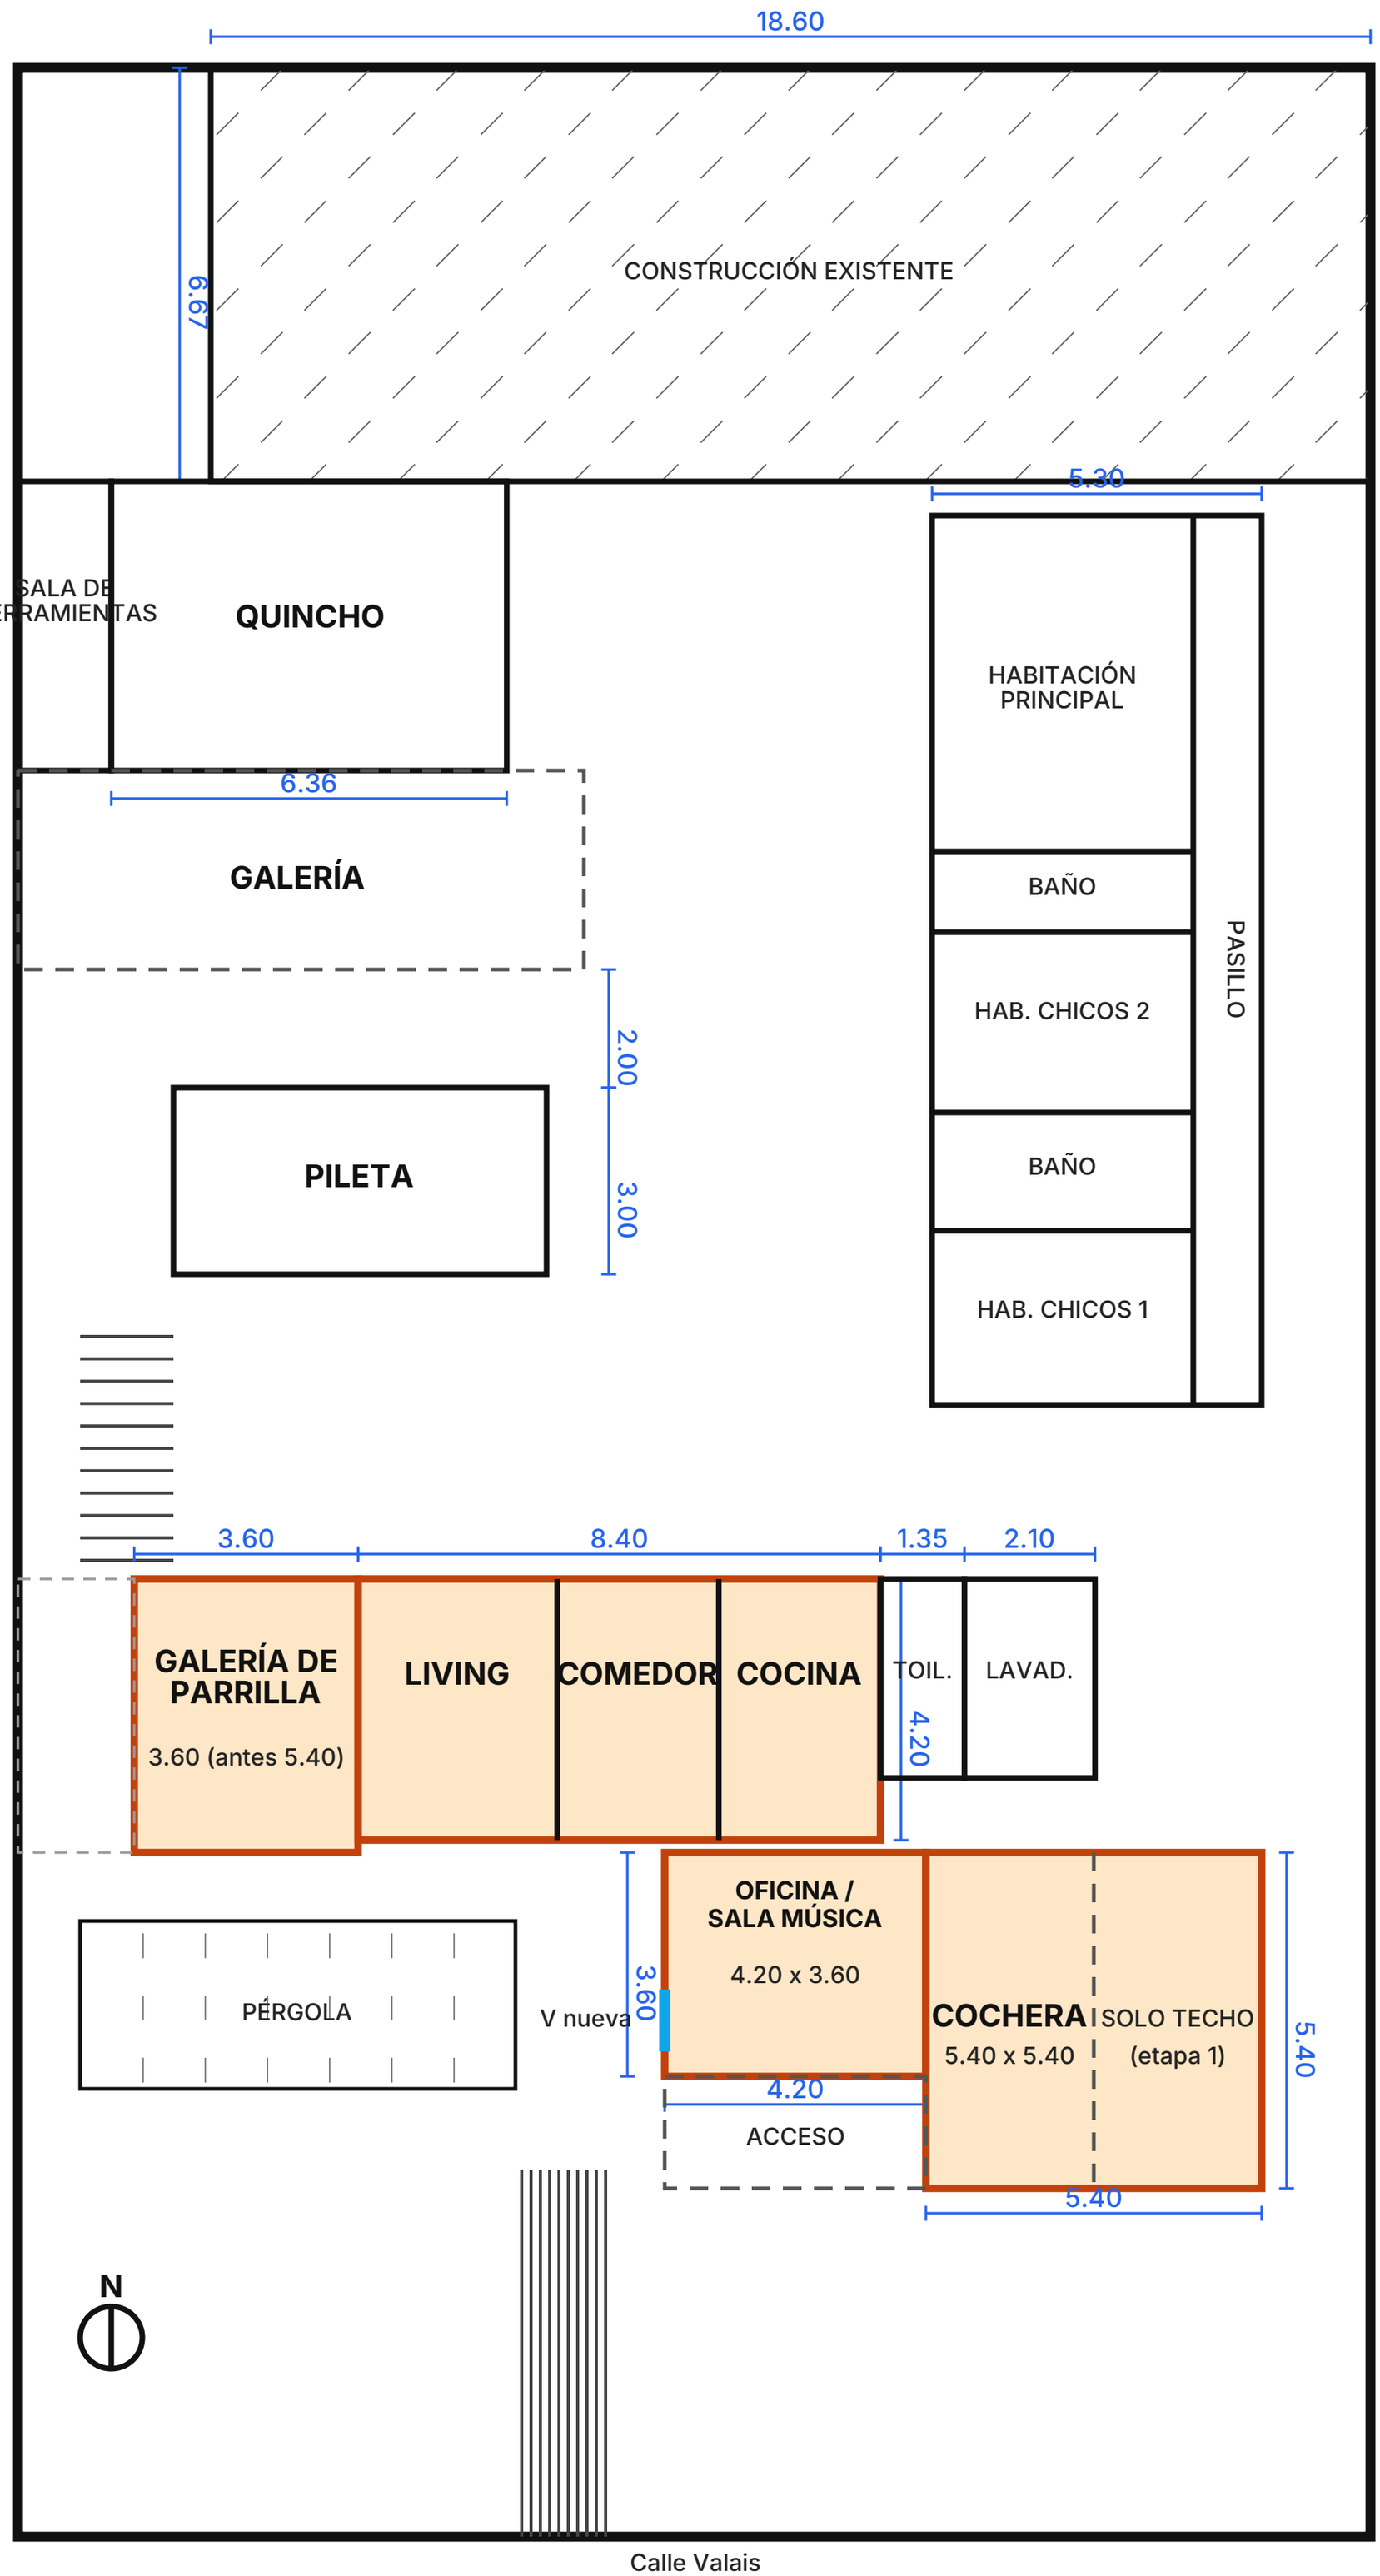

REFERENCIAS

- Ambiente modificado
- Muro / existente sin cambios
- Límite / solo techo
- Pérgola / hachurado

MEDIDAS NUEVAS

Living-comedor-cocina: 9.60 x 4.20 -> 8.40 x 4.20

(-1.20 m de largo; se corre toilette y lavadero)

Oficina/sala de música: 2.90 x 6.00 -> 4.20 x 3.60

(ventana de cochera reubicada a muro oeste)

Cochera: 5.82 x 6.00 -> 5.40 x 5.40 (solo techo)

Galería de parrilla: 5.40 -> 3.60 de largo

(se mantiene pegada al living)

CÁLCULO DE PLACAS (DURLOCK 1,20 m)

8.40 m = 7 placas exactas (sin desperdicio)

3.60 m = 3 placas exactas

4.20 m = 3 placas + 0,60 m (sobra de 0,60)

5.40 m = 4,5 placas: usar la mitad como cierre

Perfiles cada 0,60 m: 4.20, 8.40, 3.60 y 5.40 cierran

SUPERFICIES (aprox.)

Living: 40.32 -> 35.28 m2 (-5.04)

Oficina: 17.40 -> 15.12 m2 (-2.28)

Cochera: 34.92 -> 29.16 m2 (-5.76)

Galería: -1.80 m de largo (~ -7.9 m2 si prof. 4.40)

Dibujo esquemático a partir del PDF; medidas no verificadas contra el DWG original.

PLANTA GENERAL (PROPUESTA MODIFICADA - ESQUEMÁTICA)